



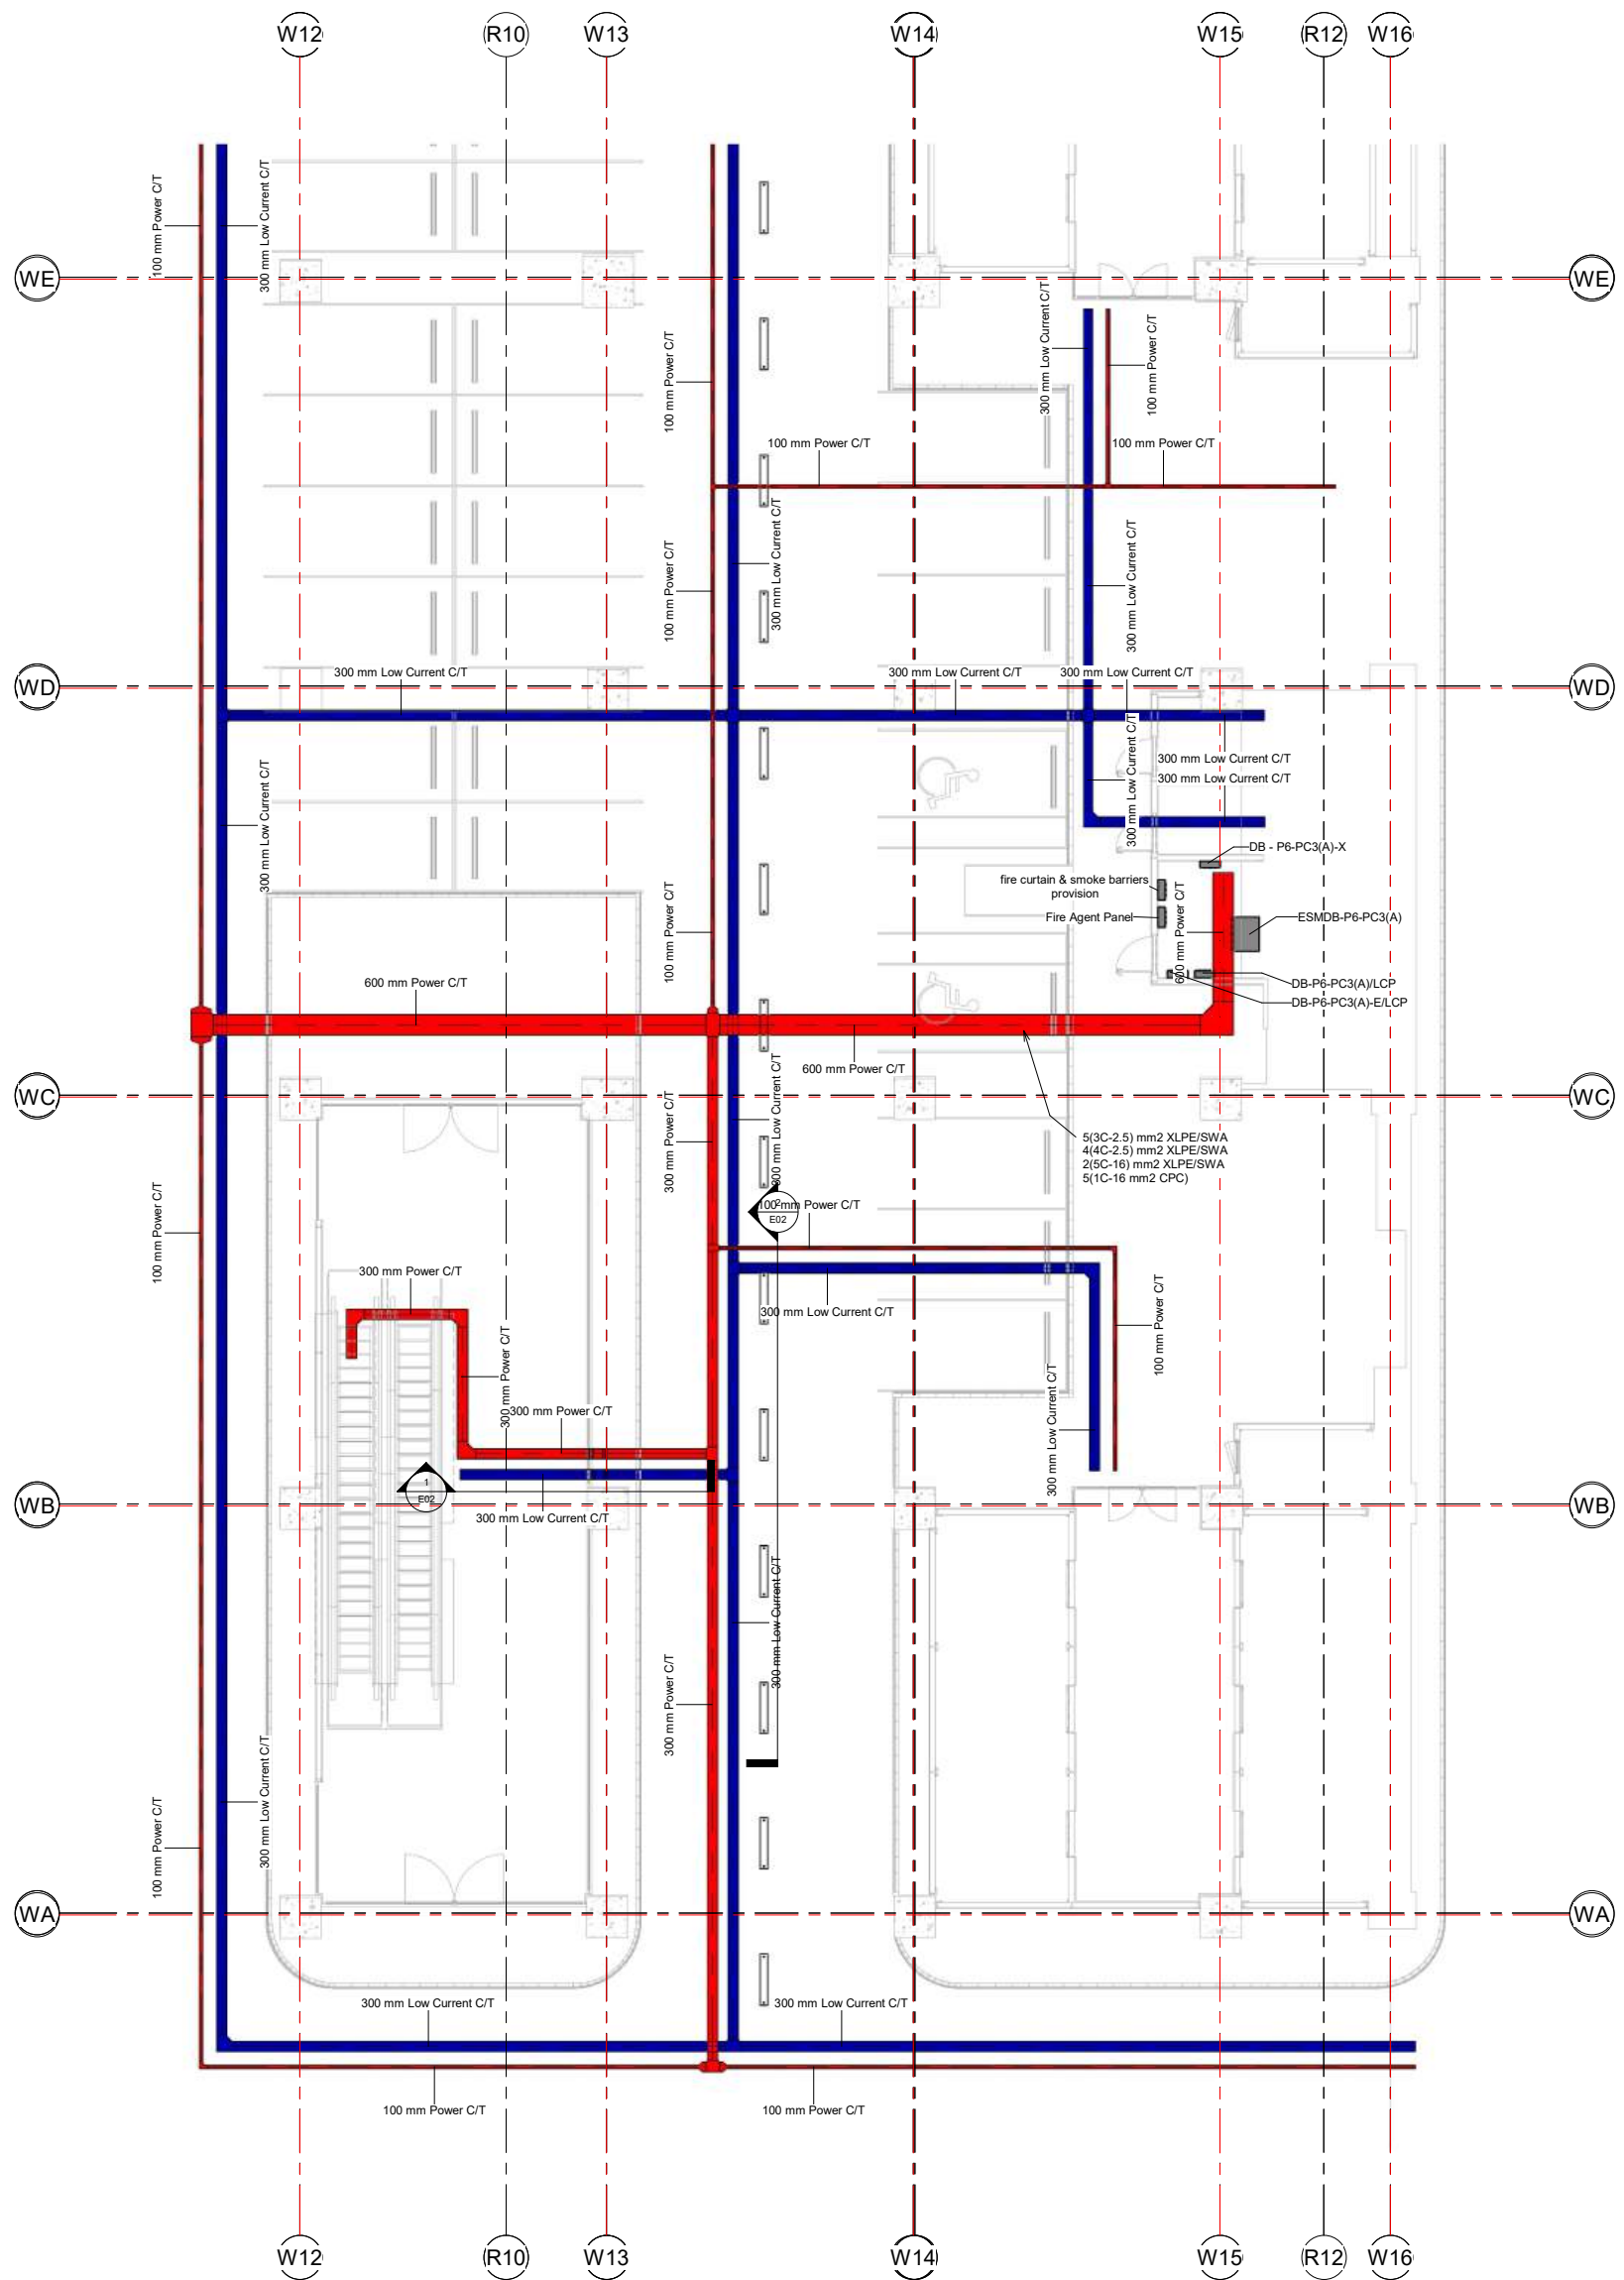


1 P06 - Cable Tray - WA/WE - W12/W16
1 : 100

E01 - PO6 - Cable Tray - 1 : 100

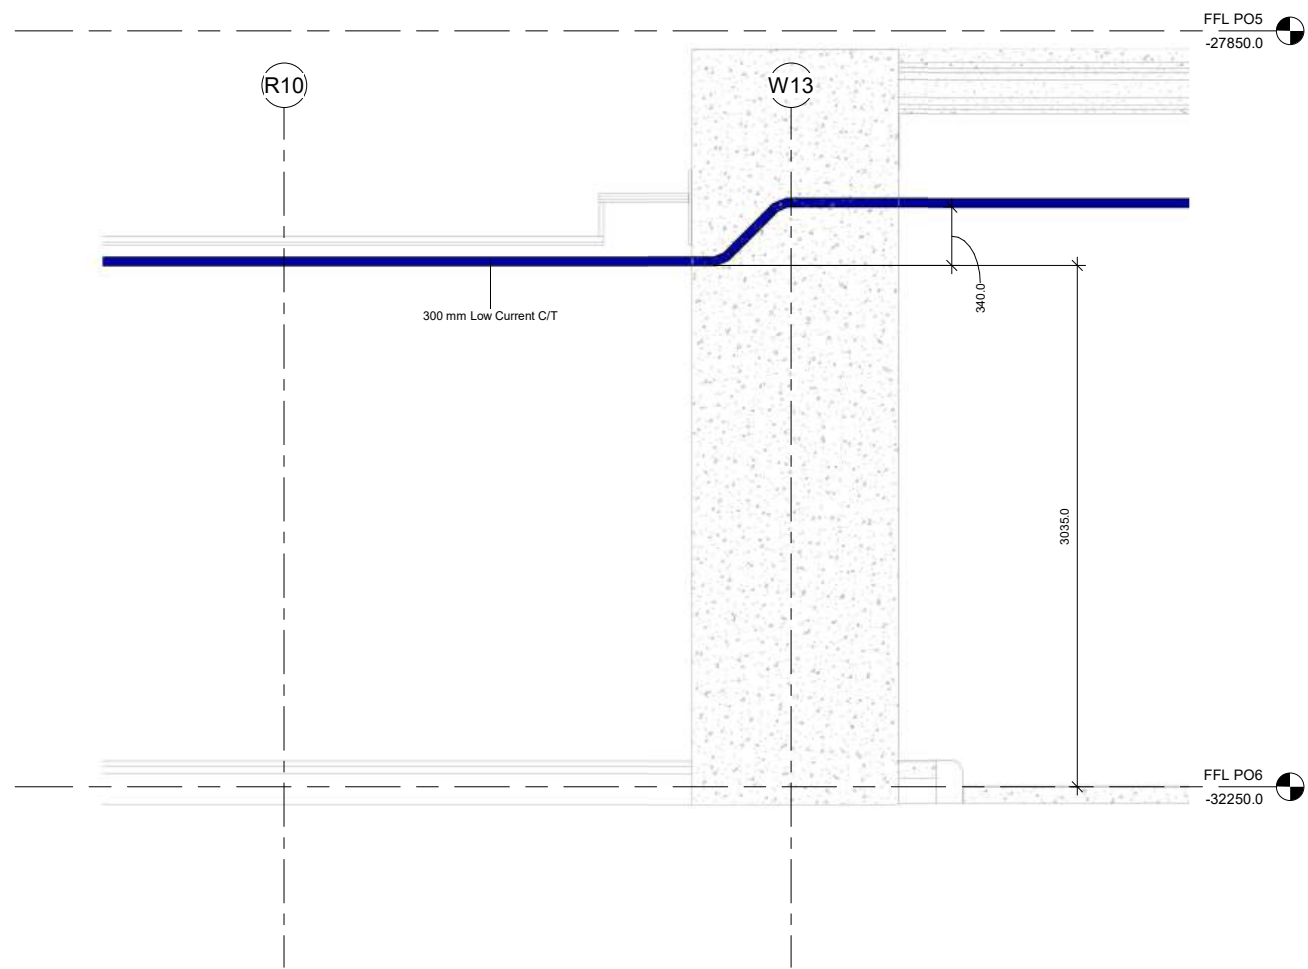


① C/T Section 1
1 : 20

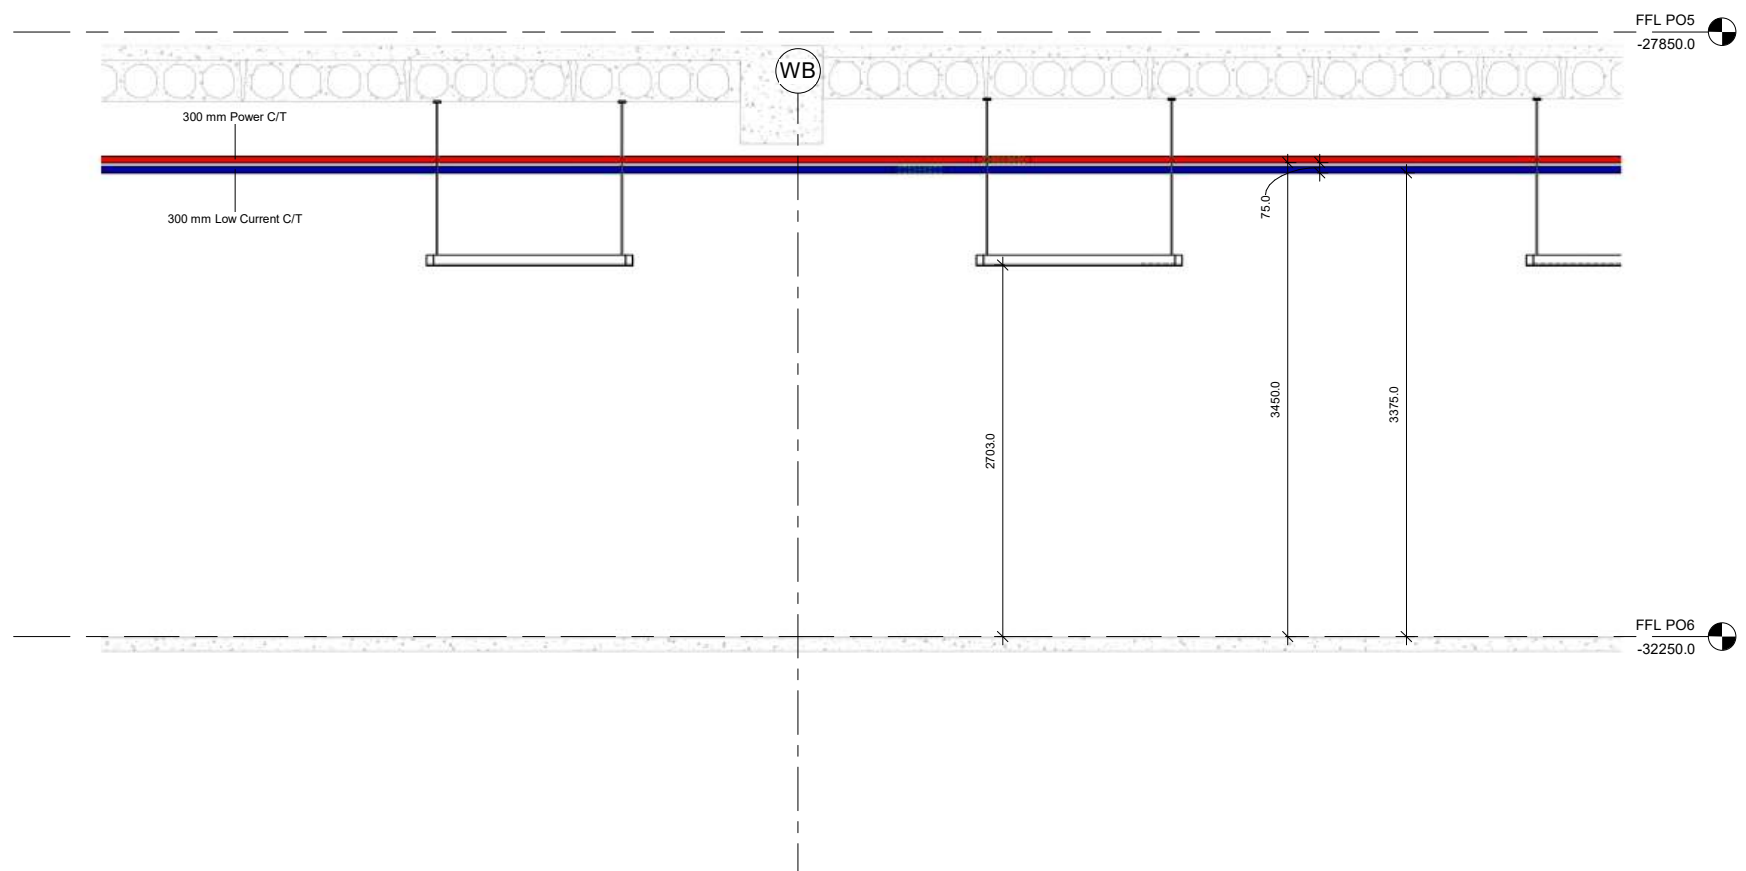



② C/T Sections 2
1 : 25

E02 - C/T Sections - As indicated

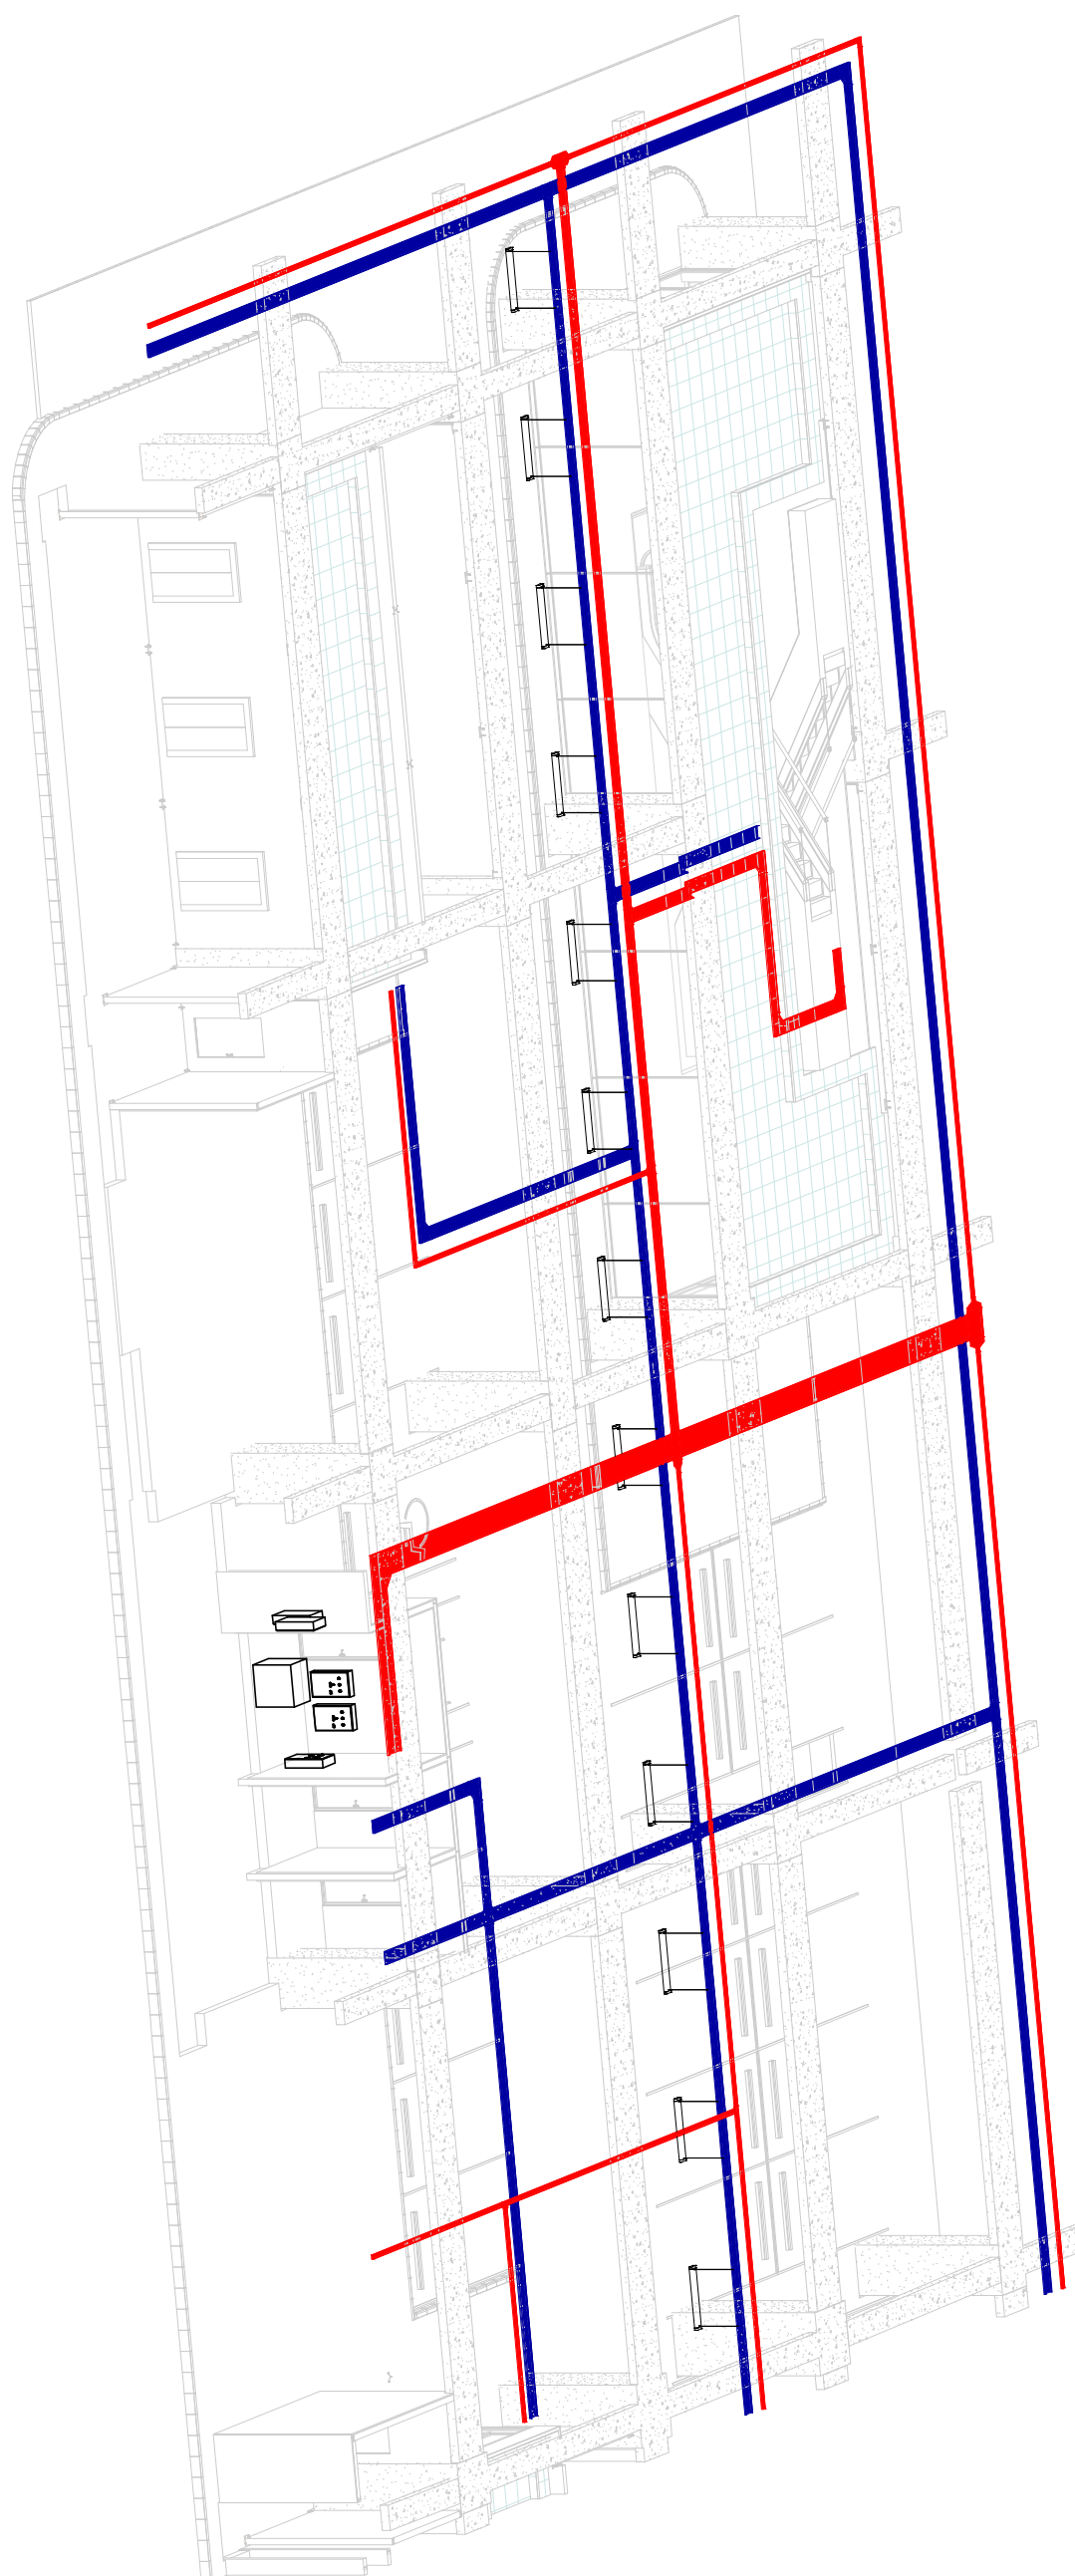



E03 - C/T 3D -

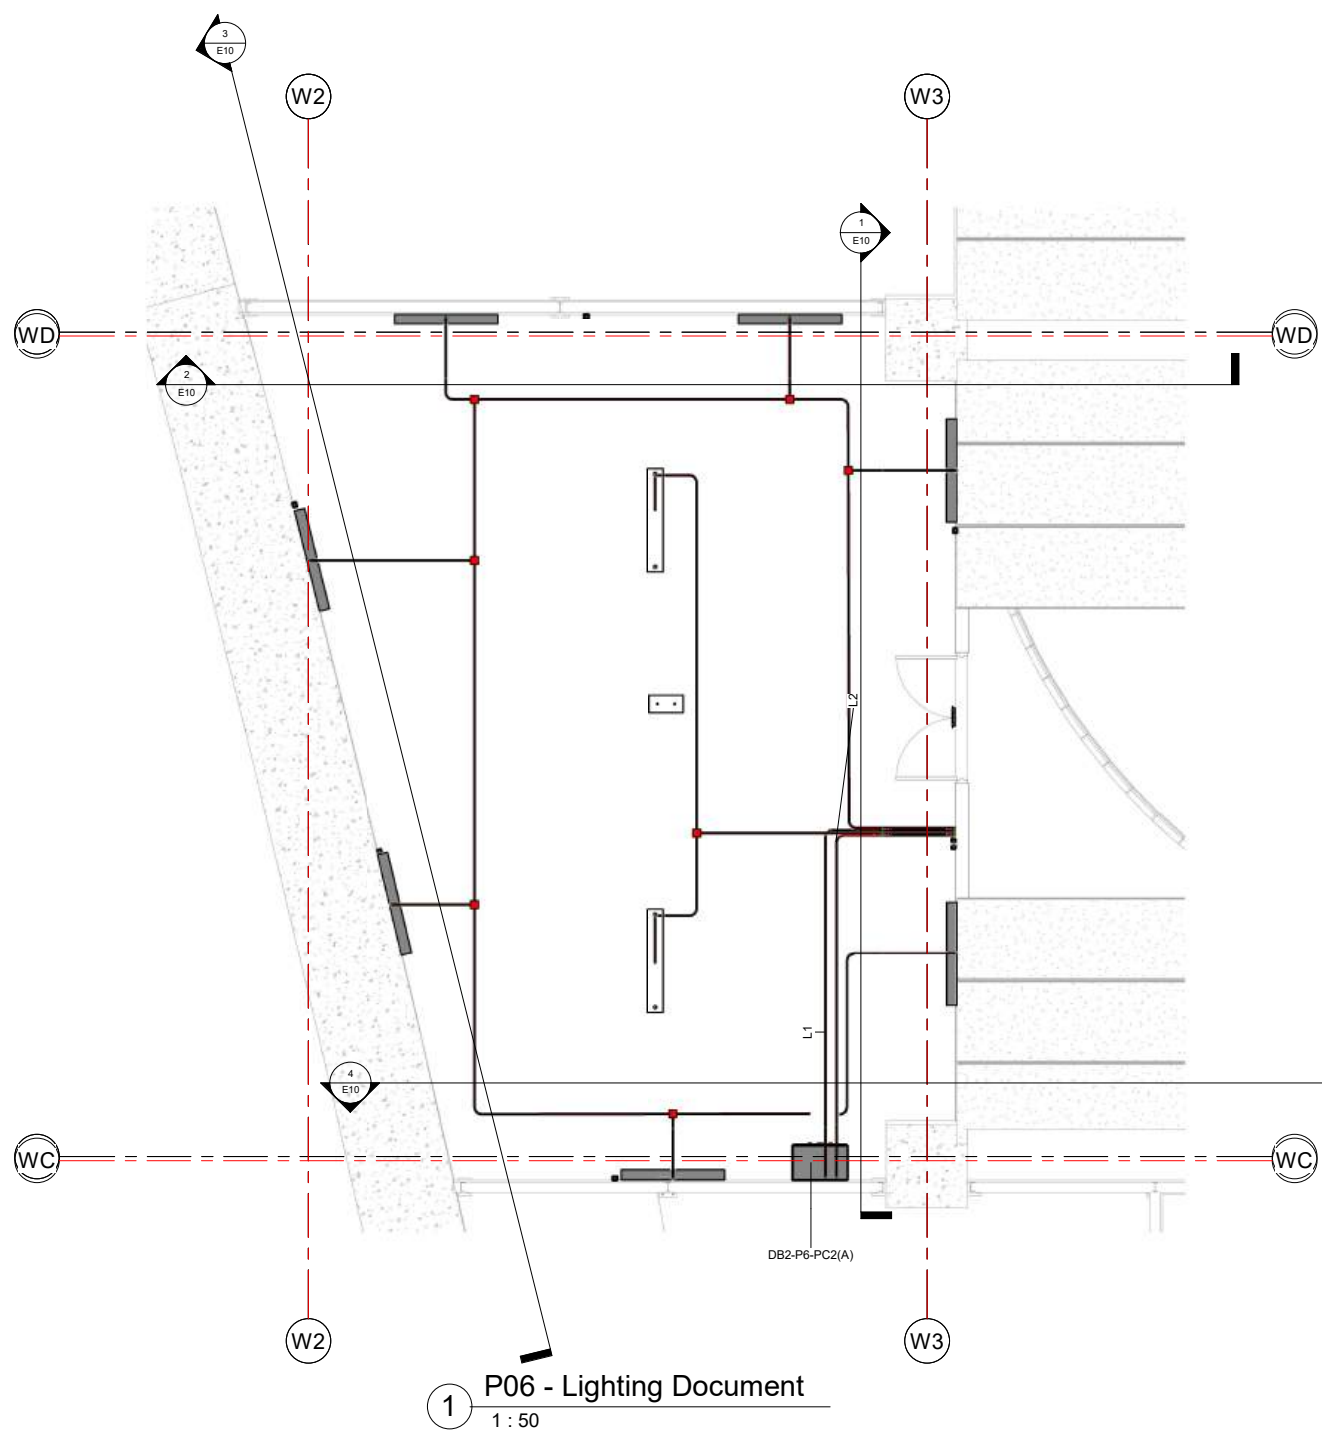


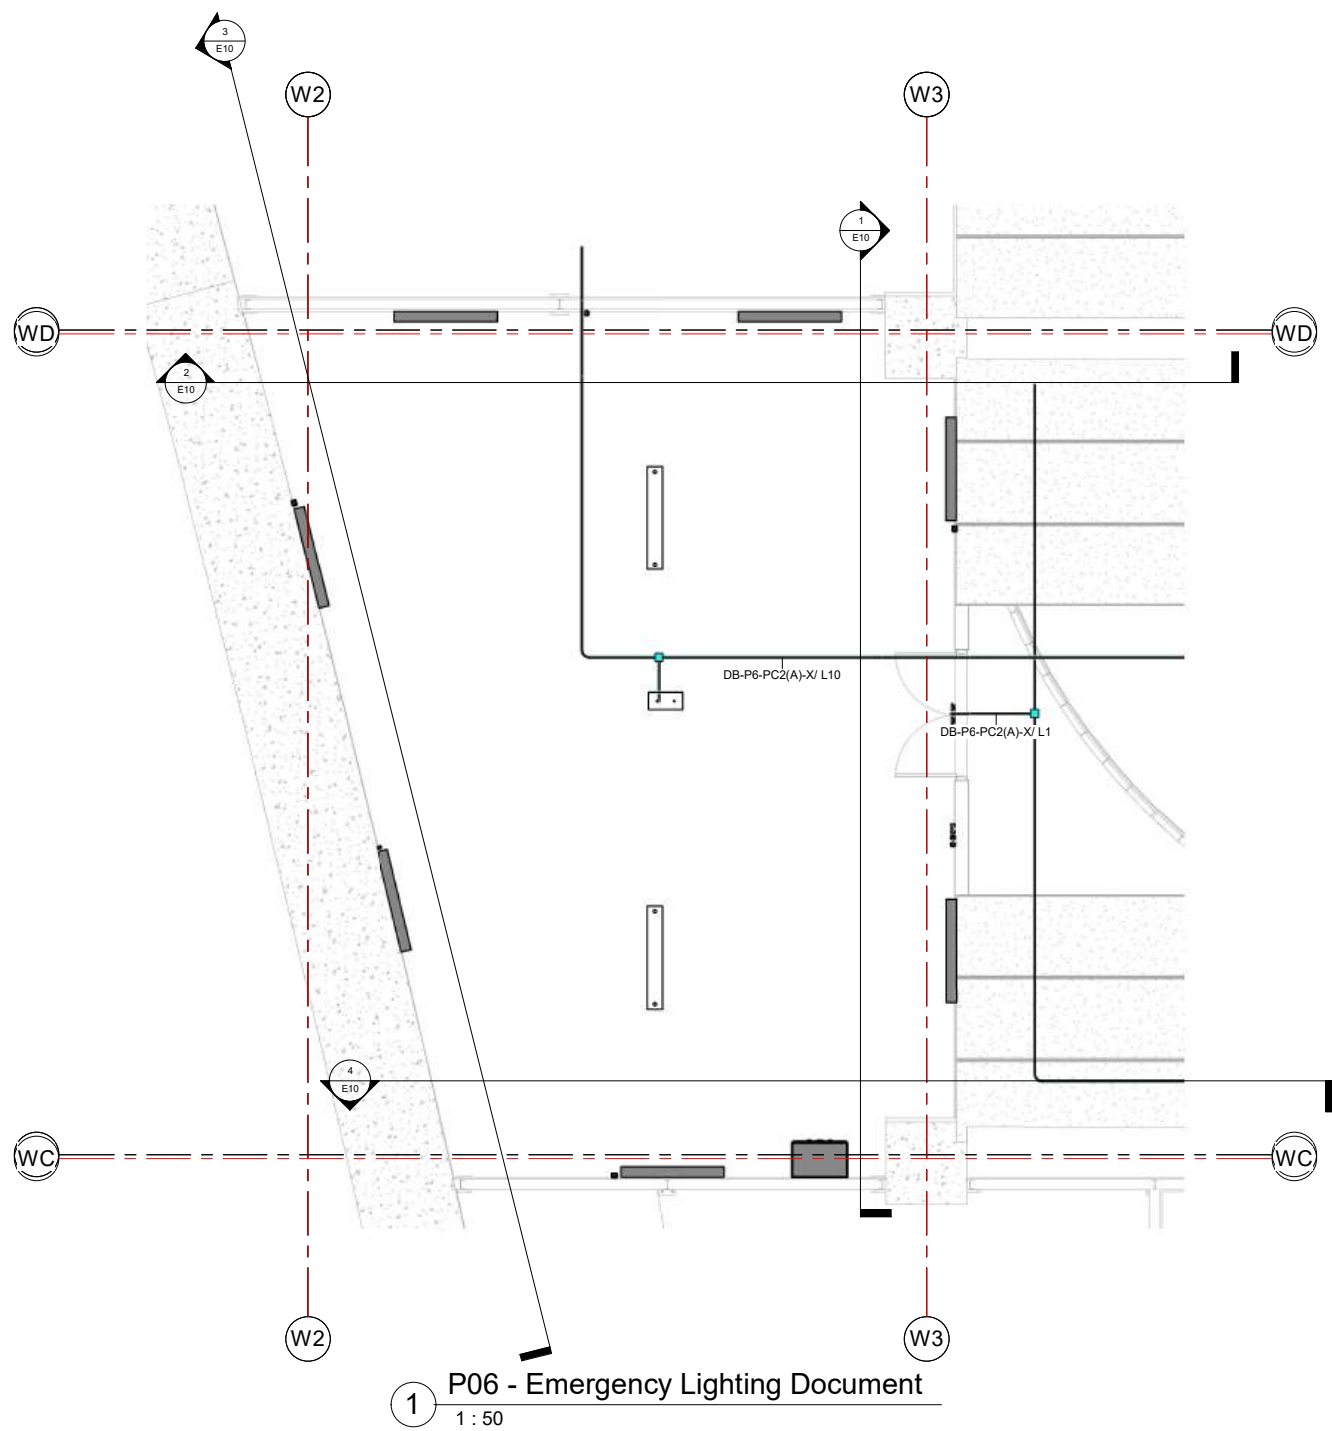




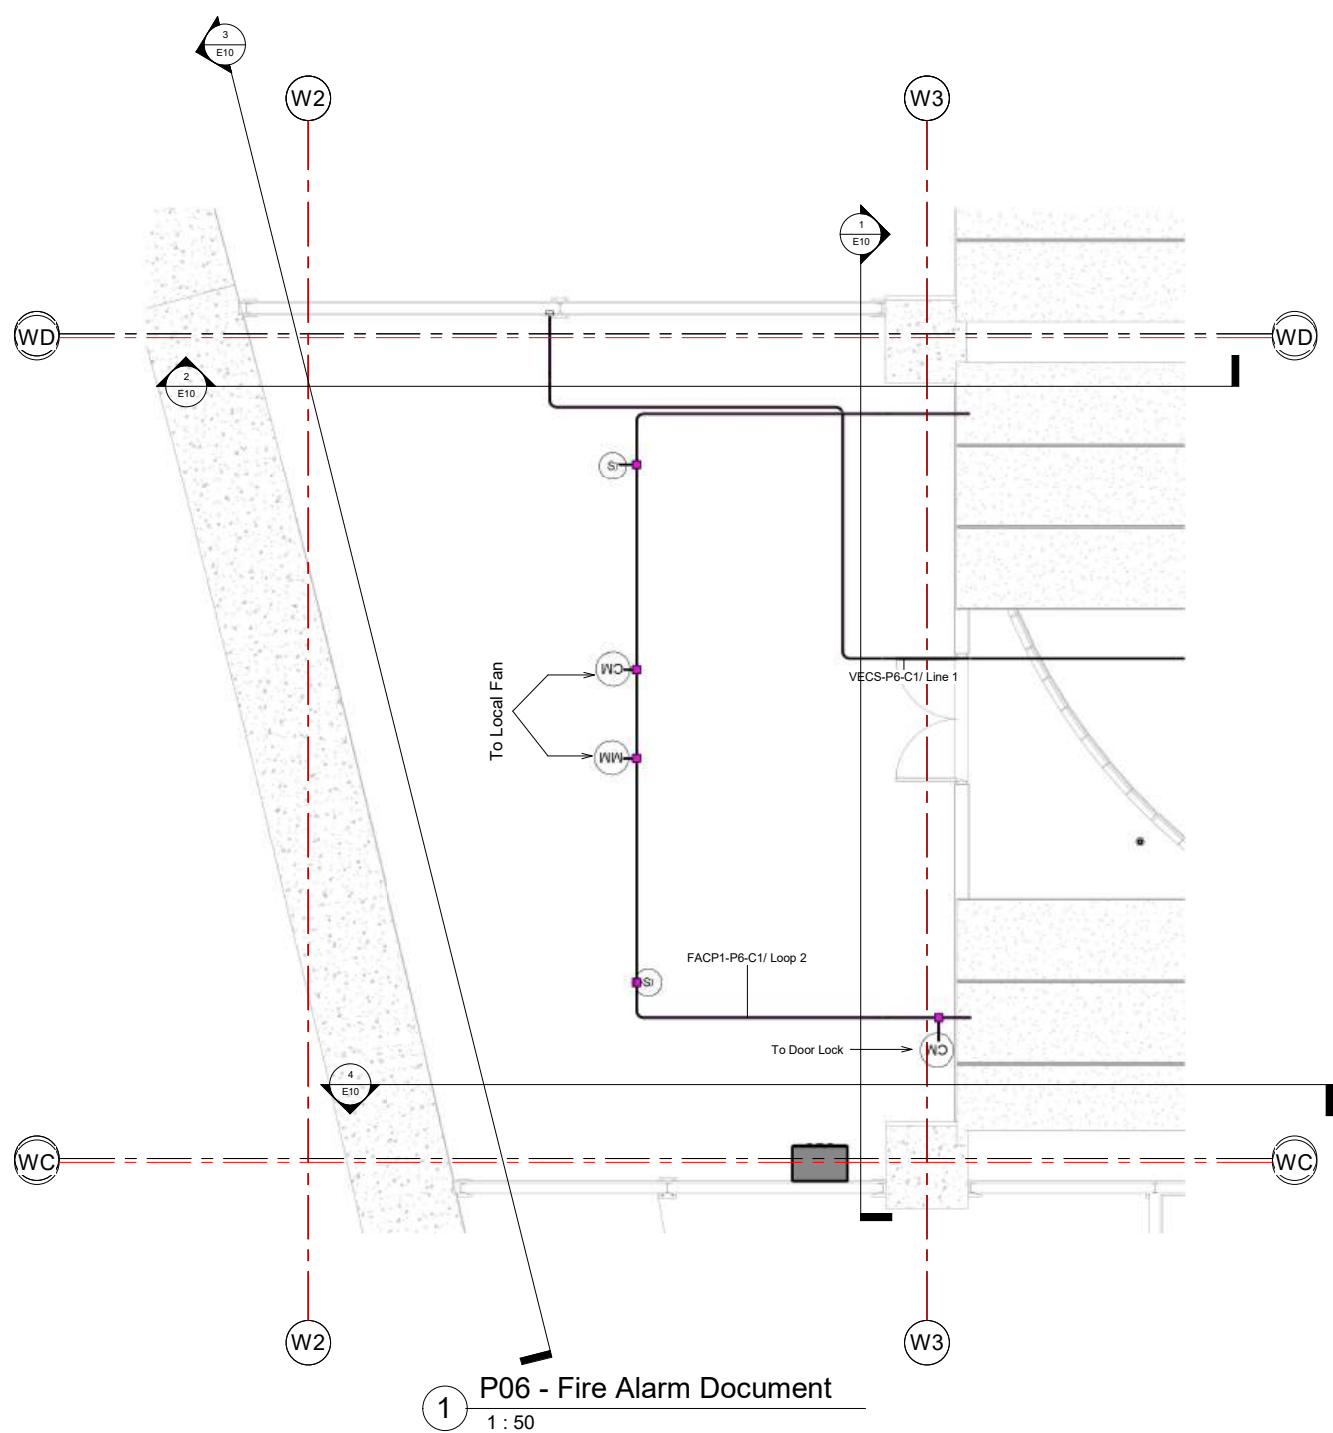


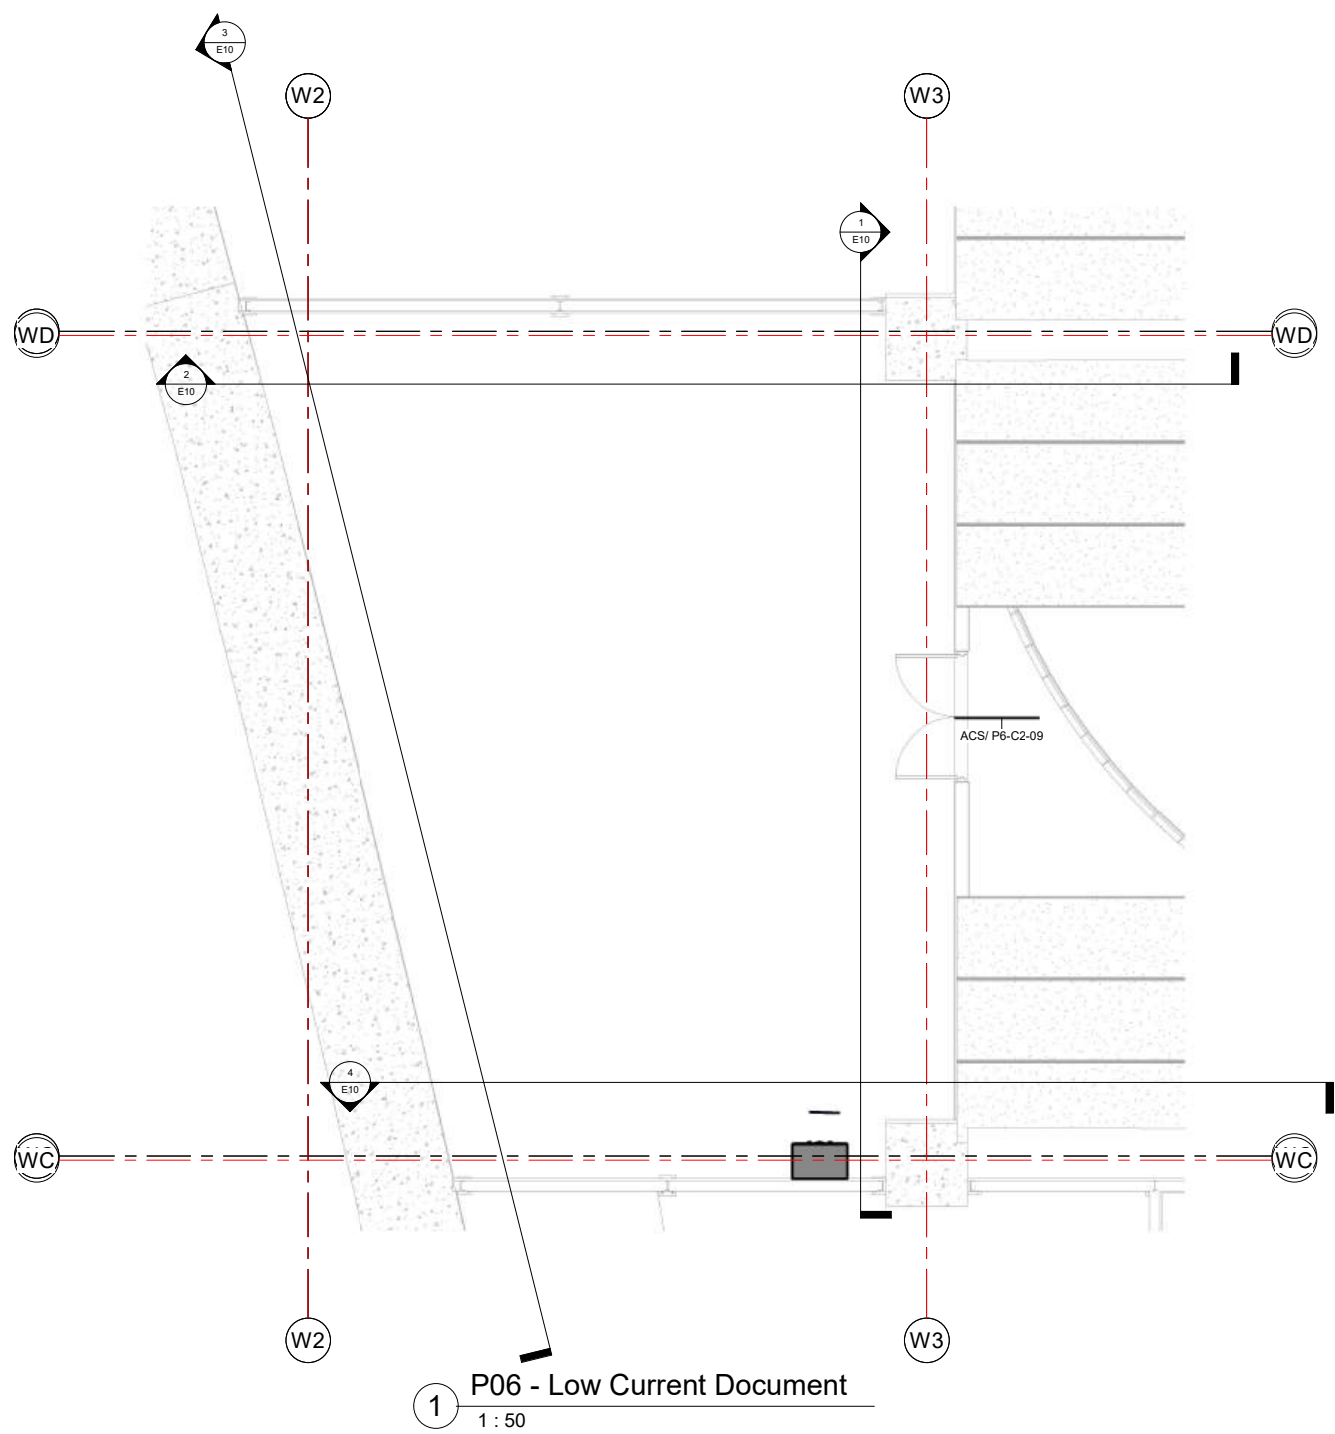

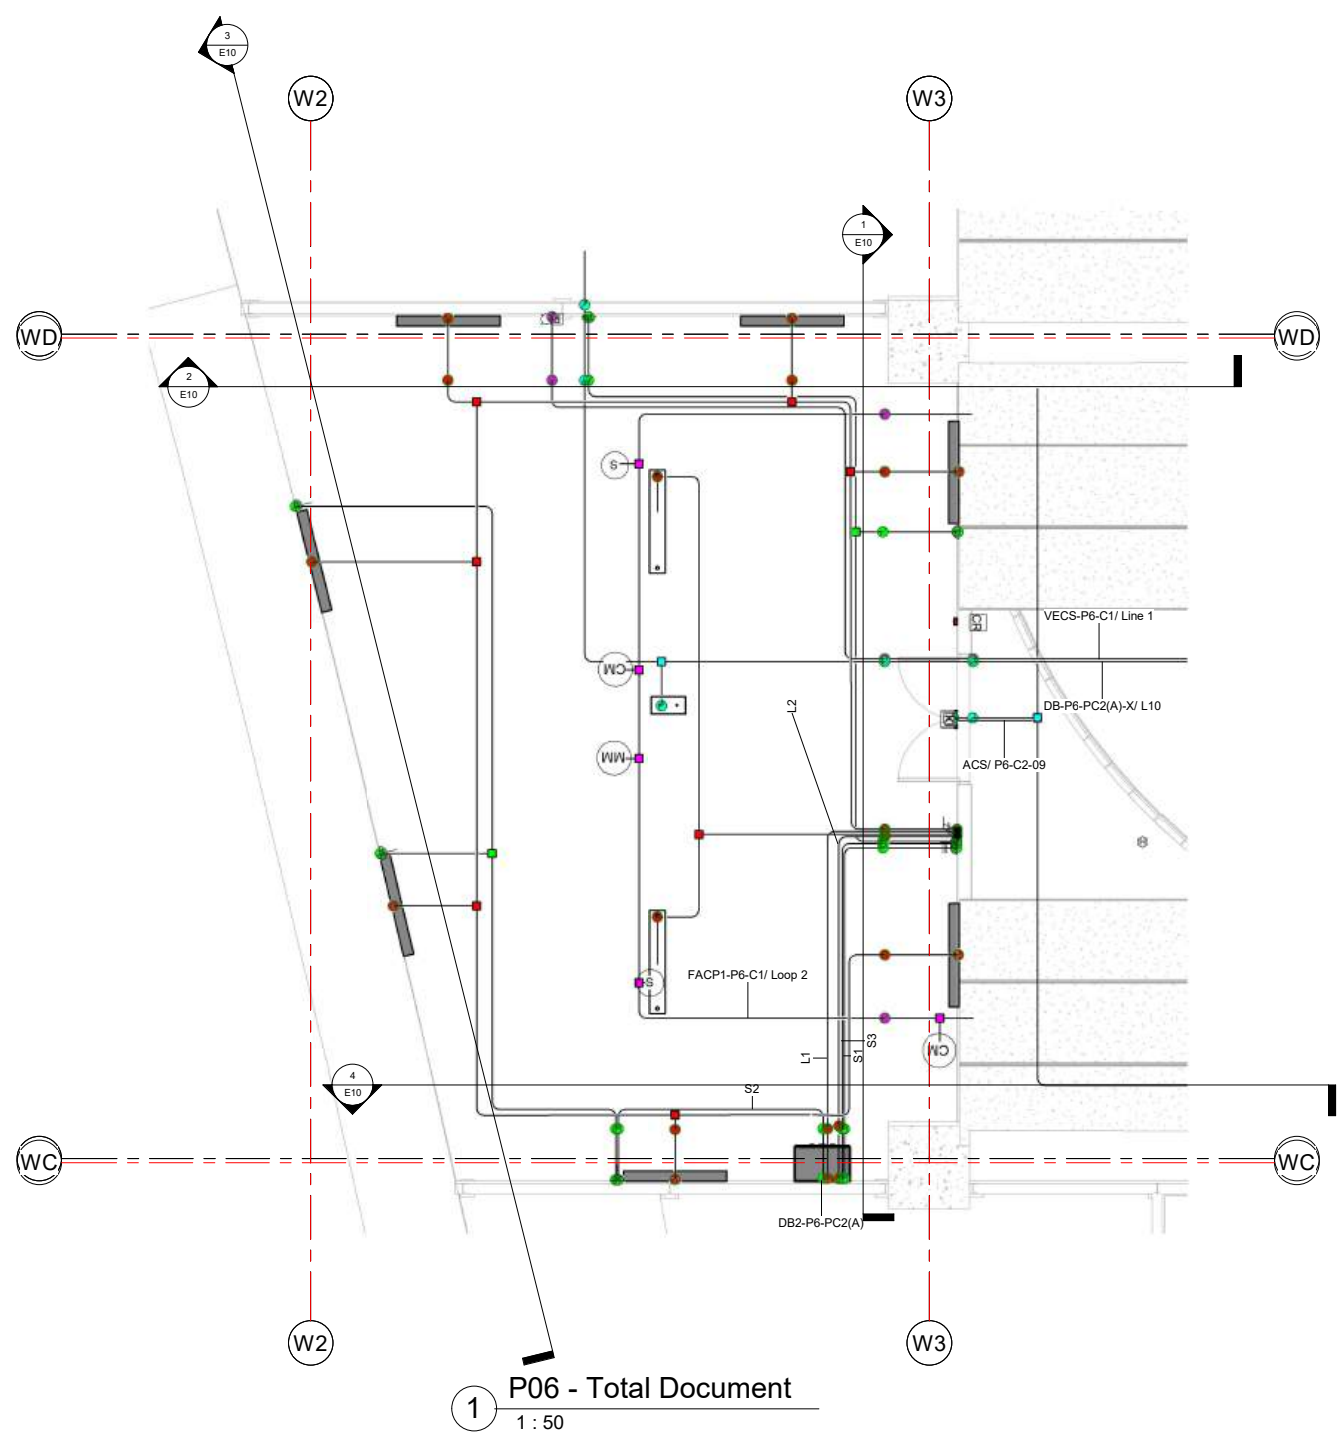


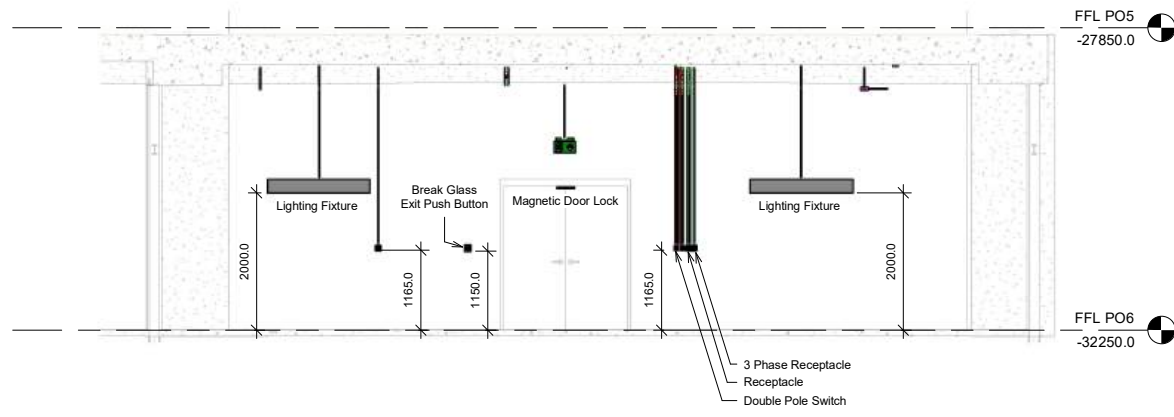


1 C/N Section 1
1 : 50

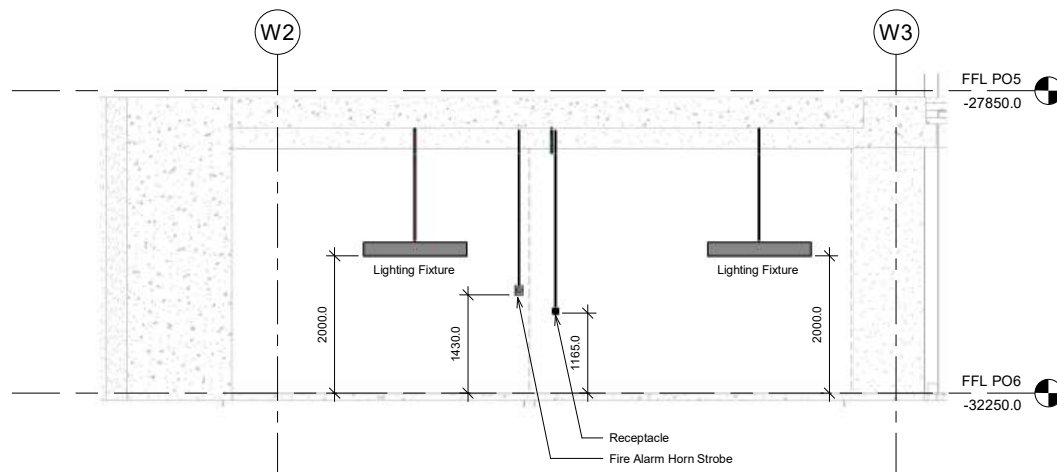


2 C/N Section 2
1 : 50

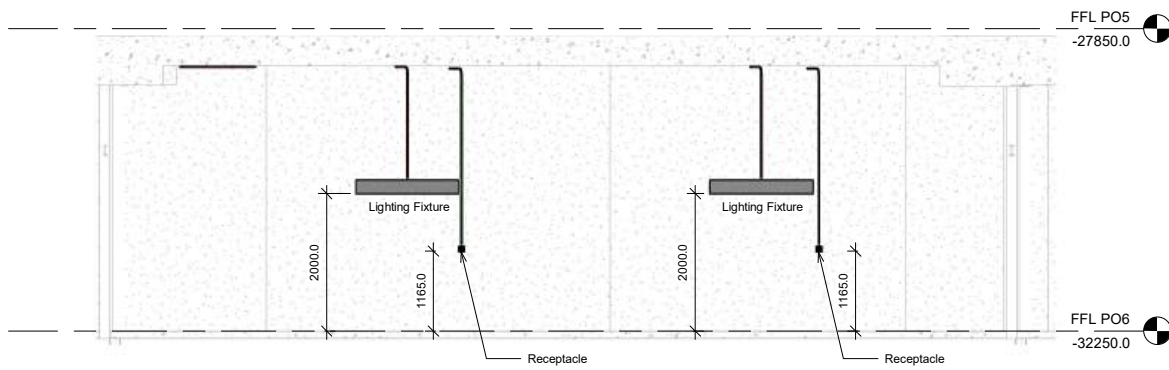

3 C/N Section 3
1 : 50




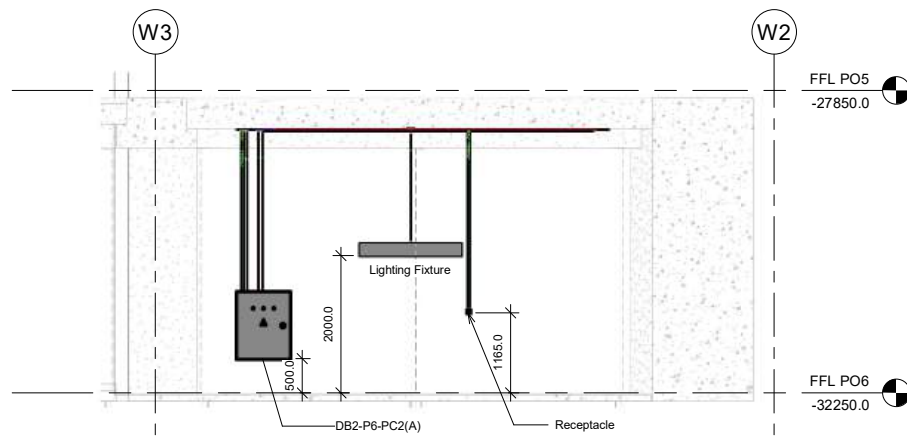



4 C/N Section 4
1 : 50

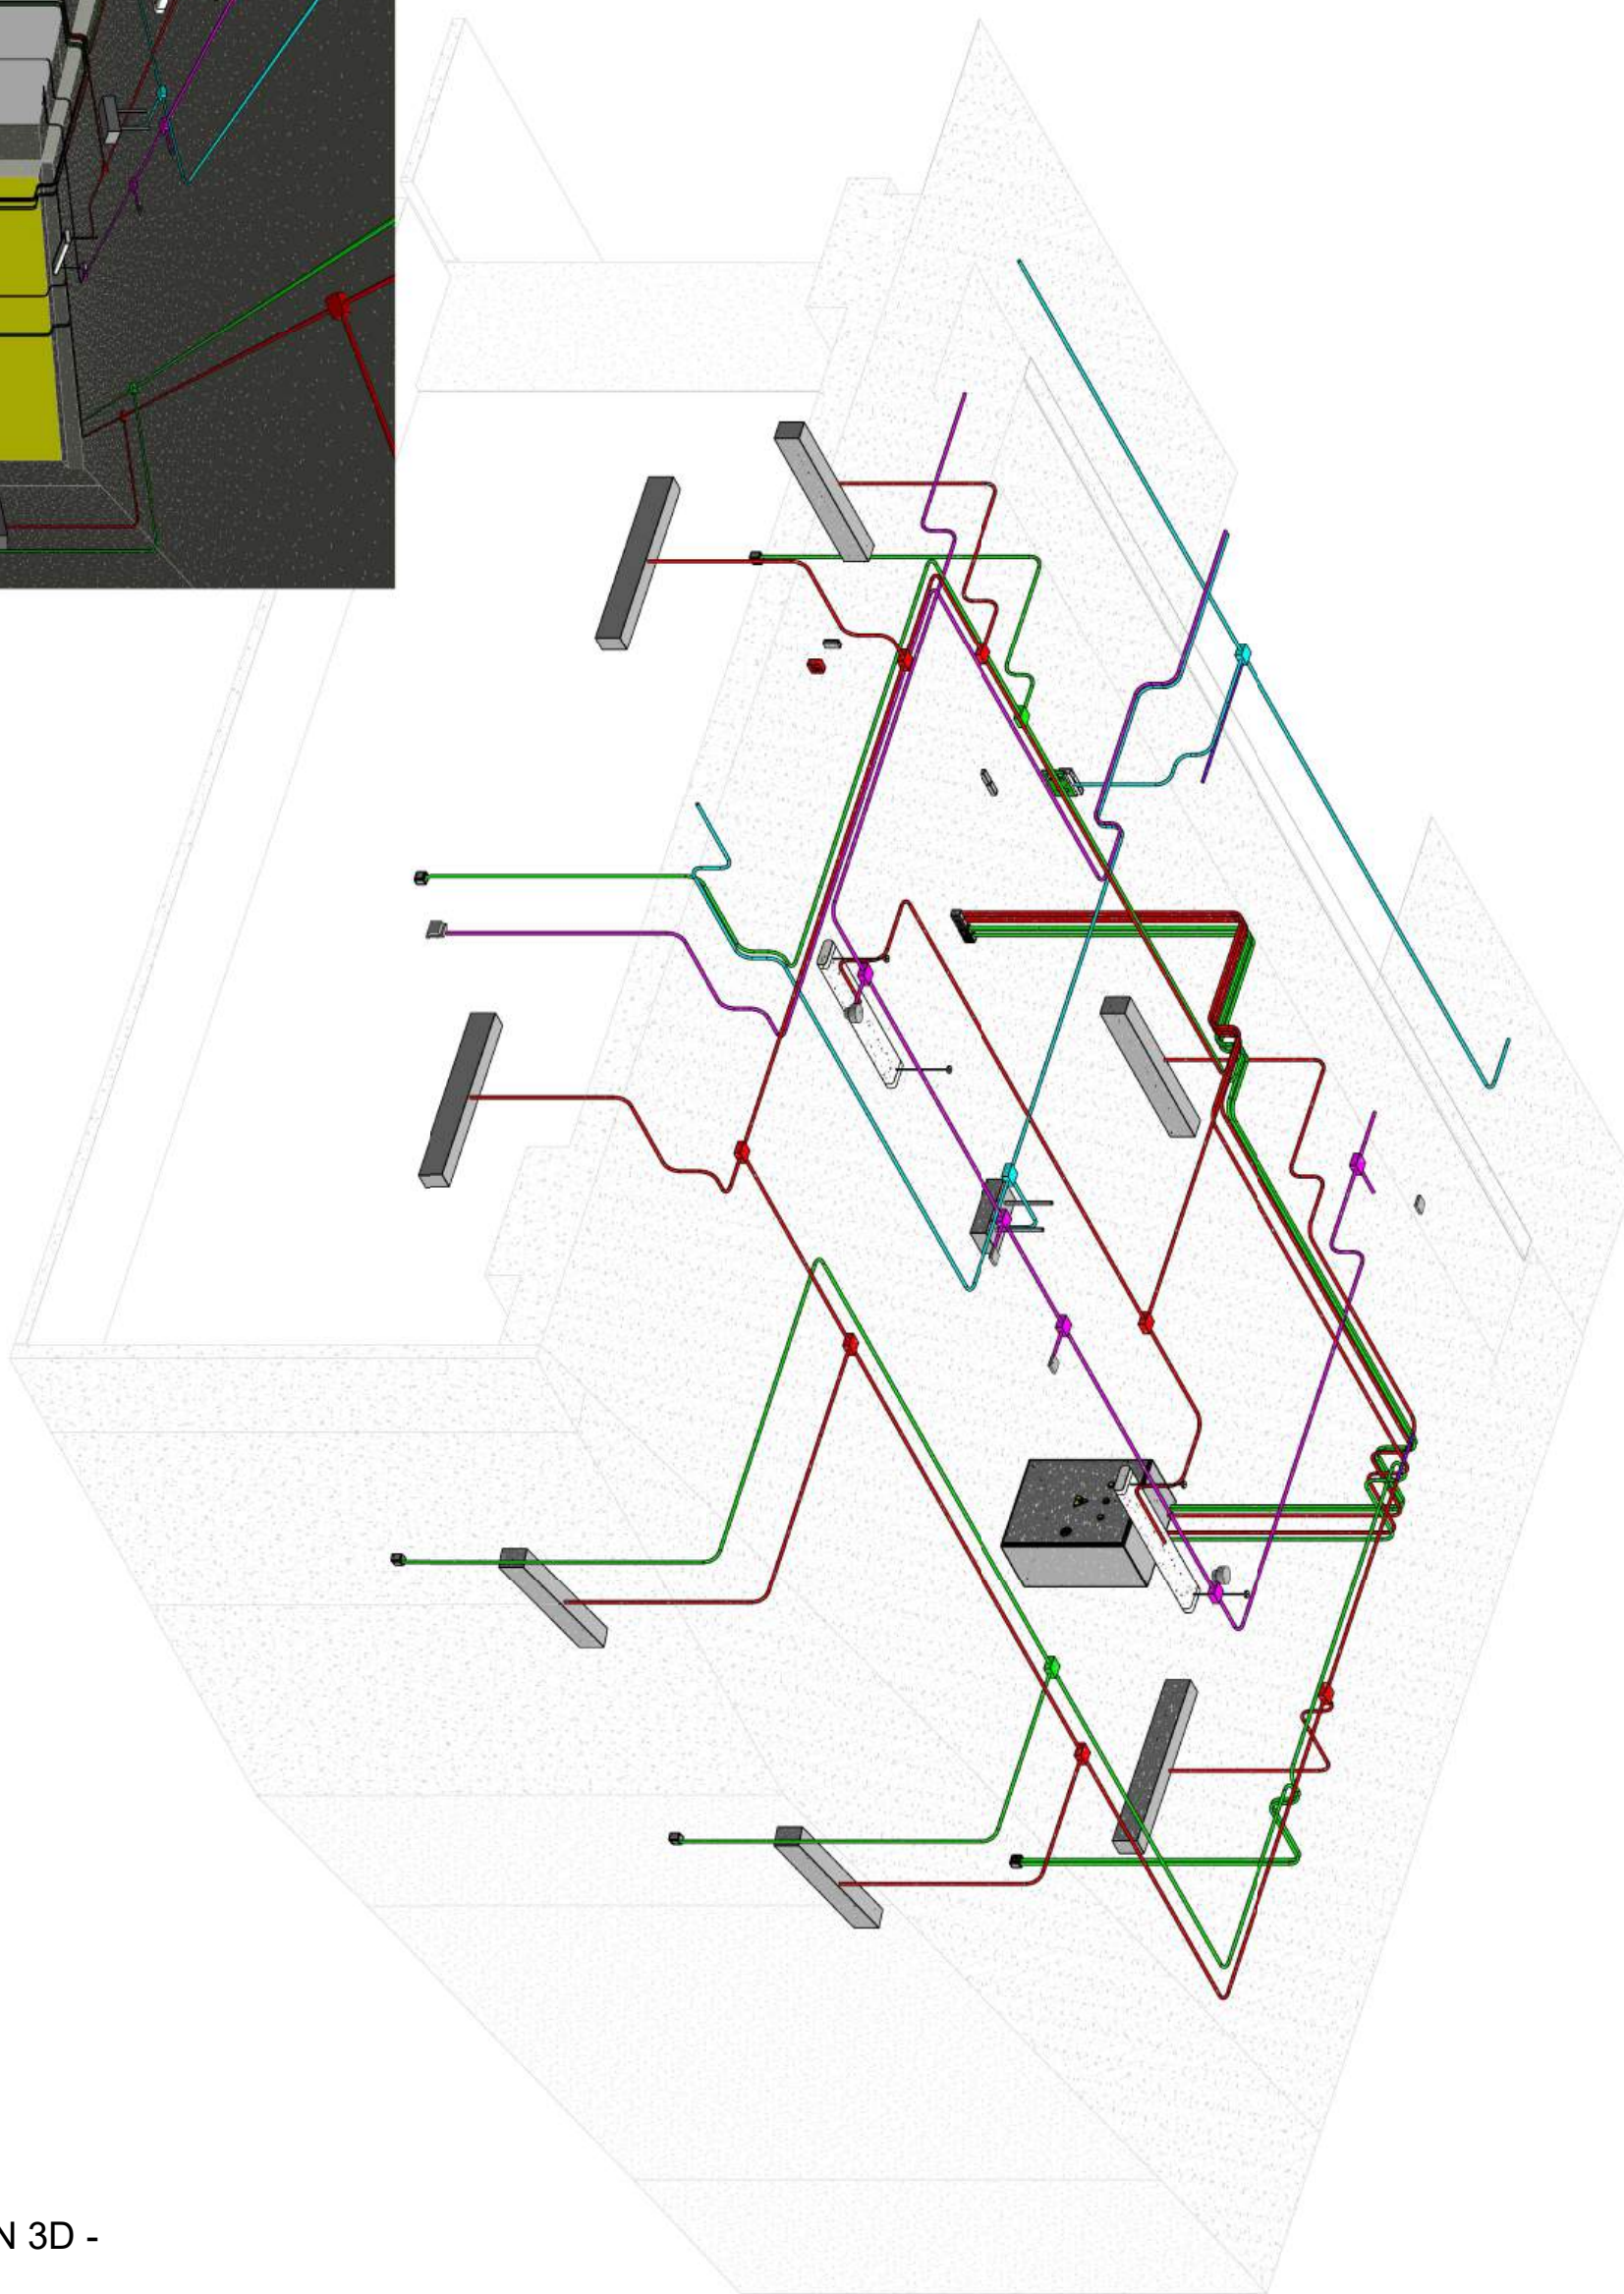

E11 - C/N 3D -

Sheet List	
Sheet Number	Sheet Name
E00	Detail & Legend
E01	PO6 - Cable Tray
E02	C/T Sections
E03	C/T 3D
E04	Lighting C/N
E05	Emergency Lighting C/N
E06	Socket C/N
E07	Fire Alarm C/N
E08	Low Current C/N
E09	Total C/N
E10	C/N Sections
E11	C/N 3D

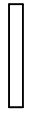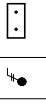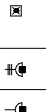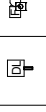Electrical Legend	
Symbols	Description
	SURFACE / RECESSED LED LIGHT FIXTURE / 58W 6000 LUMEN / IP-65
	WALL MOUNTED LED LIGHT FIXTURE / 58W 6000 LUMEN / IP-65
	WALL/SURFACE MOUNTING HIGH BAY LED TYPE EMERGENCY LUMINAIRE/8W 900 LUMEN
	ONE WAY , TWO GANG SWITCH , 10 A , 250 V
	WALL/SURFACE MOUNTED TYPE LED EXIT LUMINAIRE (LOCATION: EXIT DOORS)/8W 400 LUMEN
	16A, THREE PHASE SOCKET OUTLET
	16A, SINGLE SWITCHED SOCKET OUTLET
	ANALOGUE ADDRESSABLE SMOKE DETECTOR
	CONTROL MODULE
	MONITORING MODULE
	WALL MOUNTED SPEAKER WITH STROBE
	MAGNETIC DOOR CONTACT SUITABLE FOR DOOR TYPE (MOUNTED TOP OF DOOR)
	PROXIMITY CARD READER (CEILING MOUNTED)
	ALARMED BREAK GLASS EXIT PUSH BUTTON

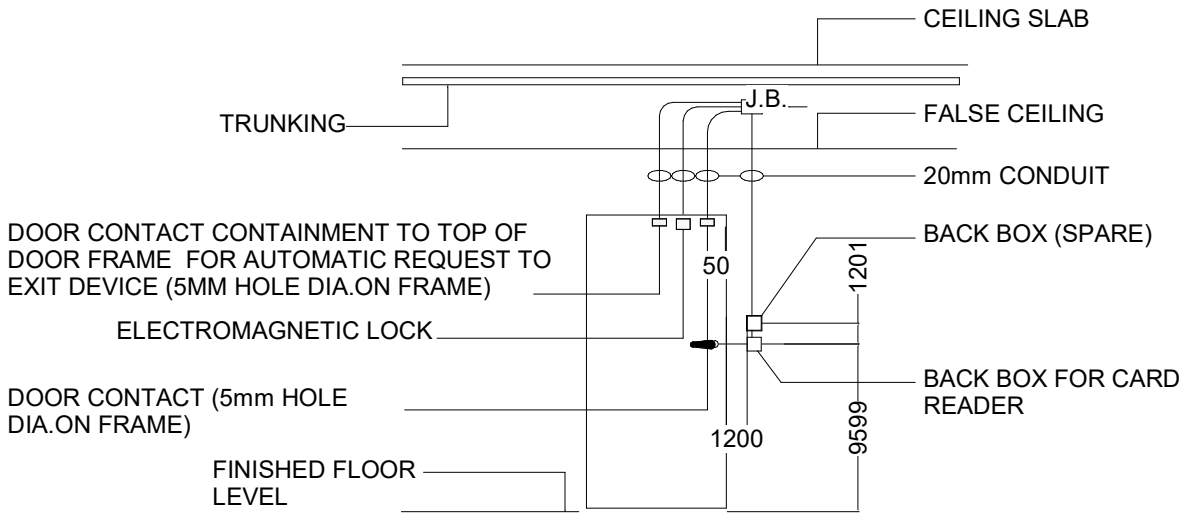

CONTAINMENT FOR ACCESS CONTROLLED
SINGLE DOOR WITH ELECTROMAGNETIC LOCK

1 Magnetic Door Lock Detail
1 : 5000