



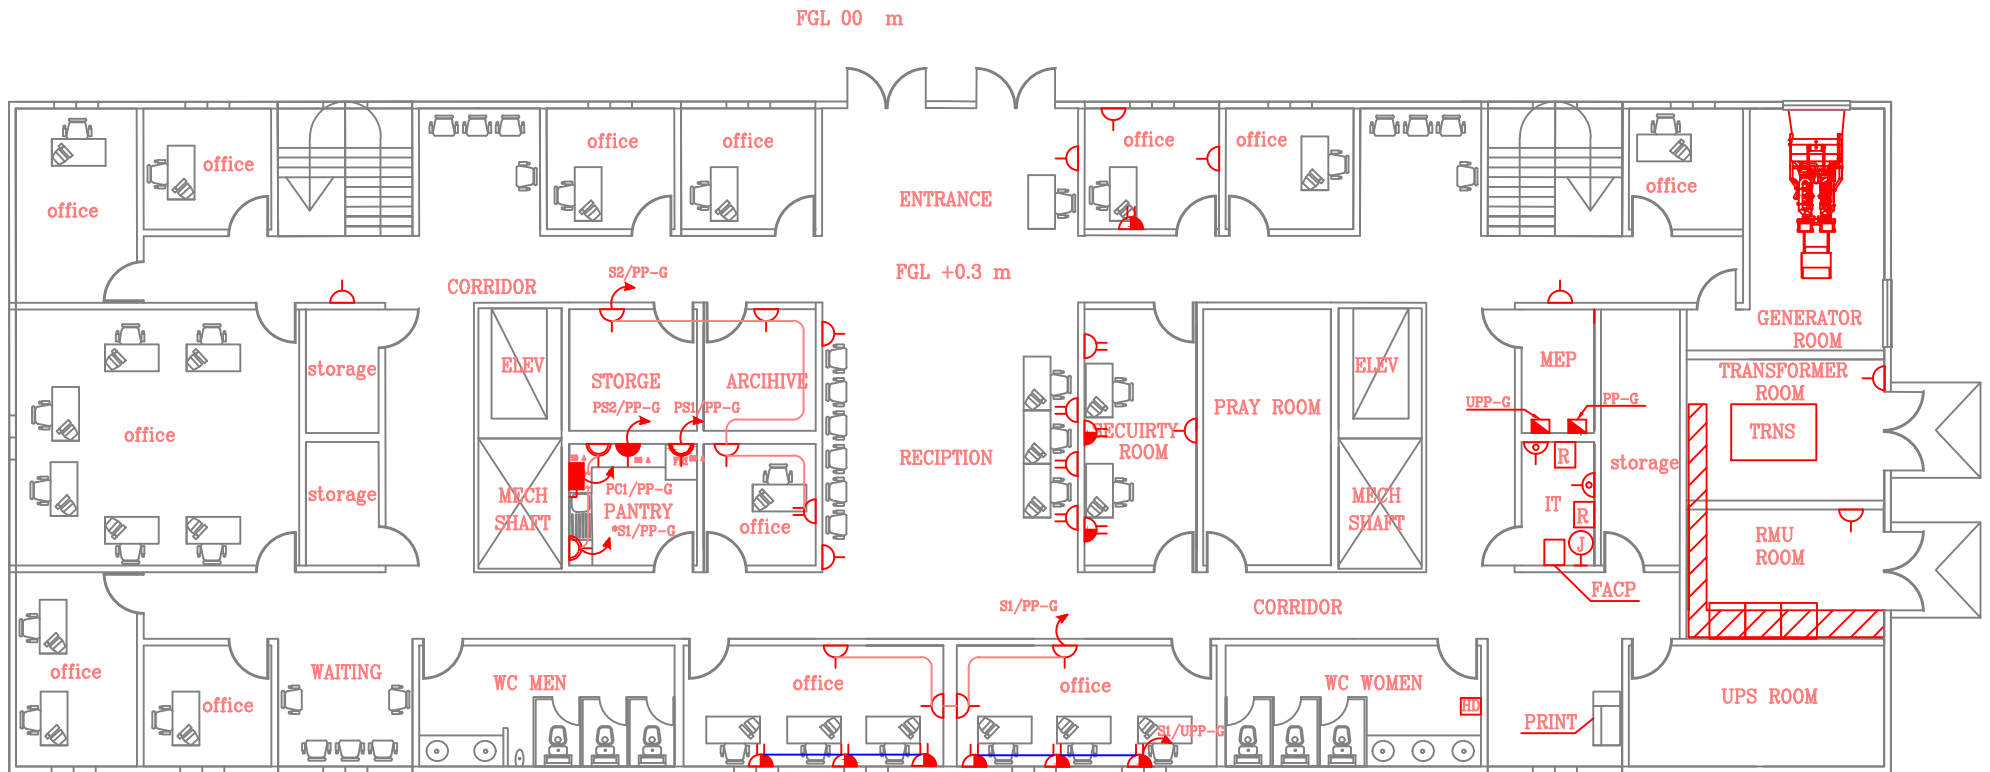

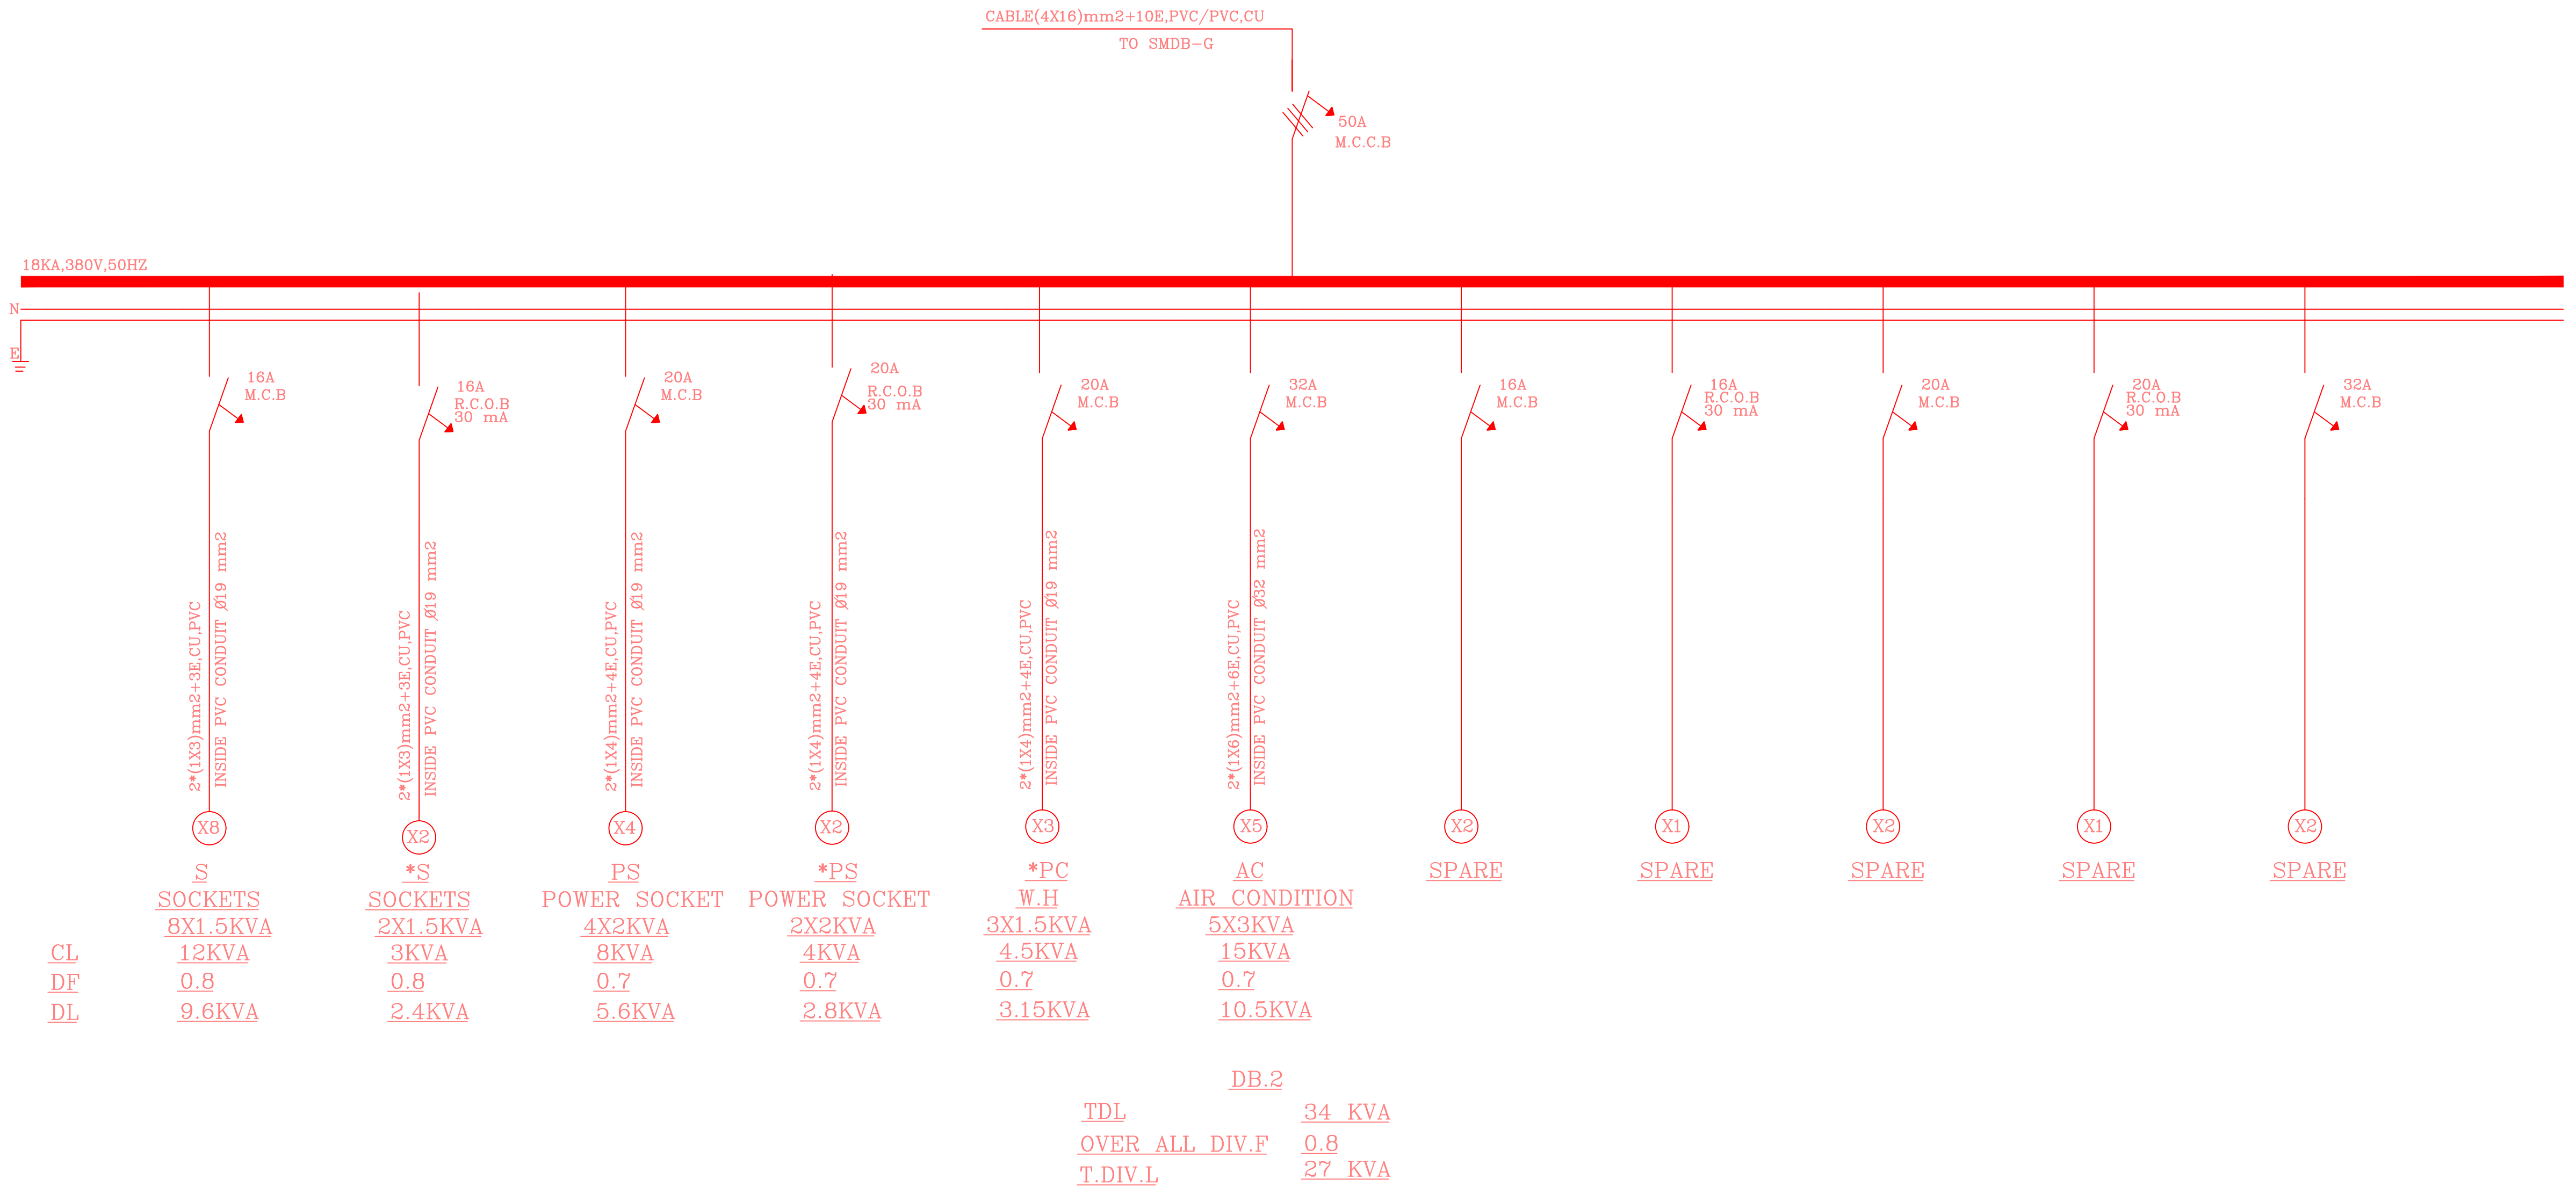

POWER LEGEND UNITS :


|     |                                                                                     |                                                                                          |
|-----|-------------------------------------------------------------------------------------|------------------------------------------------------------------------------------------|
| S1  |    | SINGLE SMALL POWER SOCKET 16 A 220 V                                                     |
| S2  |    | SAME AS S1 BUT DUBLEX TYPE                                                               |
| S3  |    | SAME AS S1 BUT WEATHER PROOF TYPE                                                        |
| S4  |    | SAME AS S1 BUT CONNECTED TO UPS                                                          |
| S5  |    | SAME AS S2 BUT WEATHER PROOF TYPE                                                        |
| S6  |    | SAME AS S2 BUT CONNECTED TO UPS                                                          |
| S7  |    | SINGLE POWER SOCKET 20 A 220 V                                                           |
| S8  |    | SAME AS S7 BUT WEATHER PROOF TYPE                                                        |
| S9  |   | SAME AS S7 BUT 380 V                                                                     |
| S10 |  | SAME AS S8 BUT 380 V                                                                     |
| S11 |  | SINGLE INDUSTRIAL POWER SOCKET WEATHER PROOF TYPE<br>220 V RATED AS SPECIFIED ON DRAWING |
| S12 |  | 3 PH INDUSTRIAL POWER SOCKET WEATHER PROOF TYPE<br>380 V RATED AS SPECIFIED ON DRAWING   |
| S13 |  | DISCONNECT SWITCH 2P 220V<br>RATED AS SPECIFIED ON DRAWING                               |
| S14 |  | DISCONNECT SWITCH 2P 220V WEATHER PROOF TYPE<br>RATED AS SPECIFIED ON DRAWING            |
| S15 |  | DISCONNECT SWITCH 4P 380V<br>RATED AS SPECIFIED ON DRAWING                               |
| S16 |  | DISCONNECT SWITCH 4P 380V WEATHER PROOF TYPE<br>RATED AS SPECIFIED ON DRAWING            |
| S18 |  | ELECTRICAL OUTLET RATED AS SPECIFIED ON DRAWING                                          |
| S19 |  | ELECTRICAL FLOOR BOX CONTAIN :<br>(1 DUPLEX 16 A NORMAL+1 DUPLEX 16 A UPS)               |
| S20 |  | ELECTRICAL FLOOR BOX CONTAIN :<br>(1 SINGLE 16 A NORMAL+1 SINGLE 16 A UPS)               |


|                                                                                       |         |
|---------------------------------------------------------------------------------------|---------|
|  | LP-X    |
|  | PP-X    |
|  | LPP-X   |
|  | ELP-X   |
|  | EPP-X   |
|  | ELPP-X  |
|  | UPP-X   |
|  | SMDB    |
|  | DB-X    |
|  | SMDB-X  |
|  | ESMDB-X |
|  | USMDB-X |







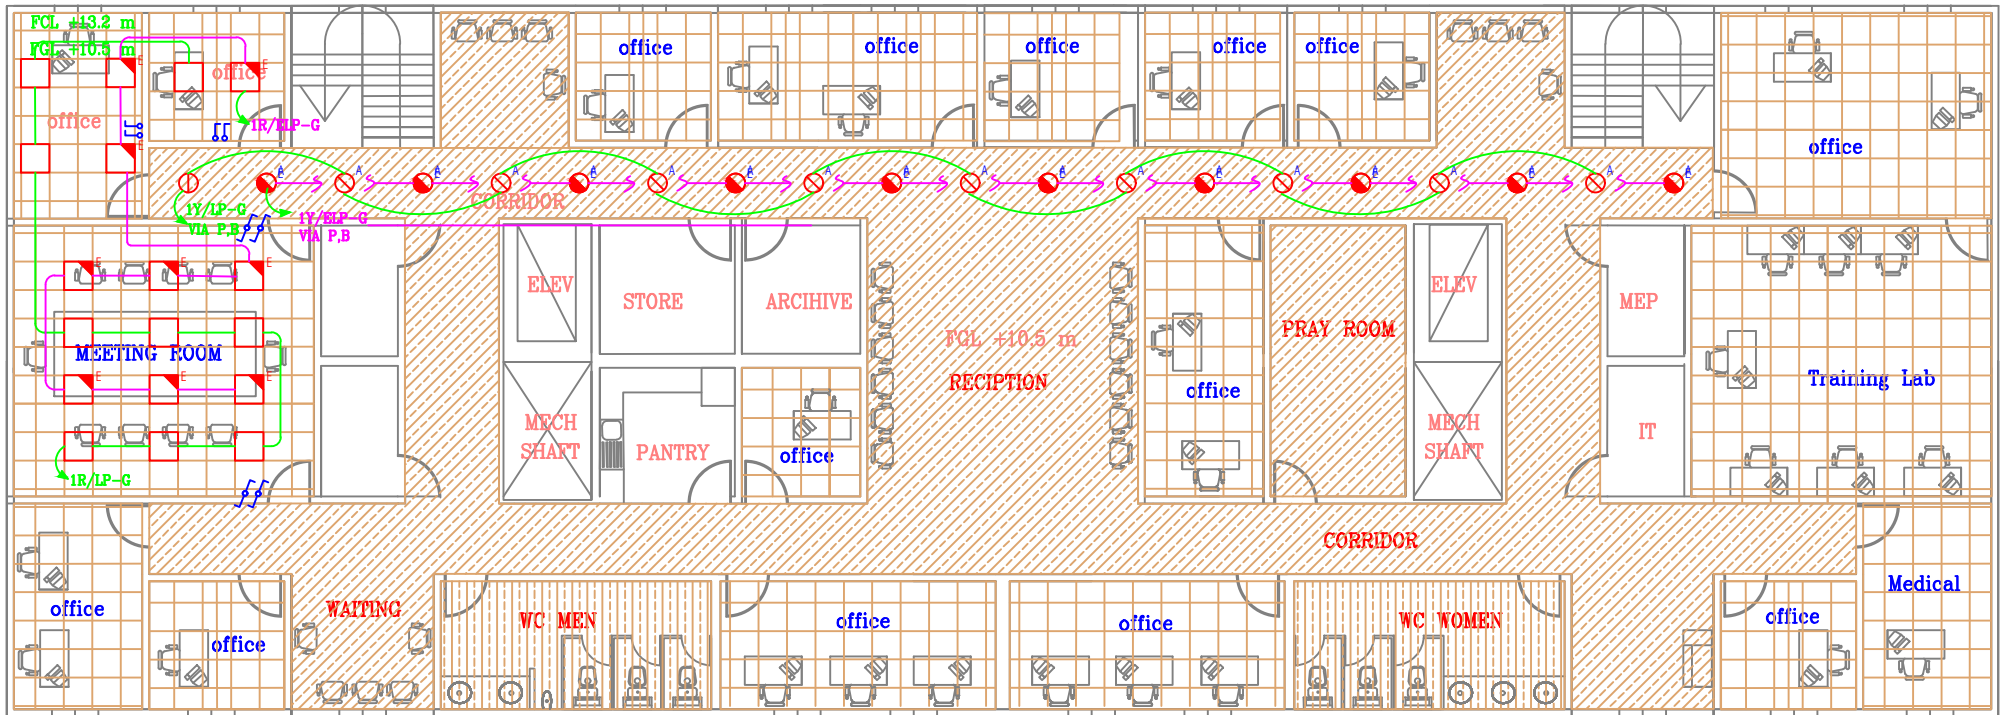

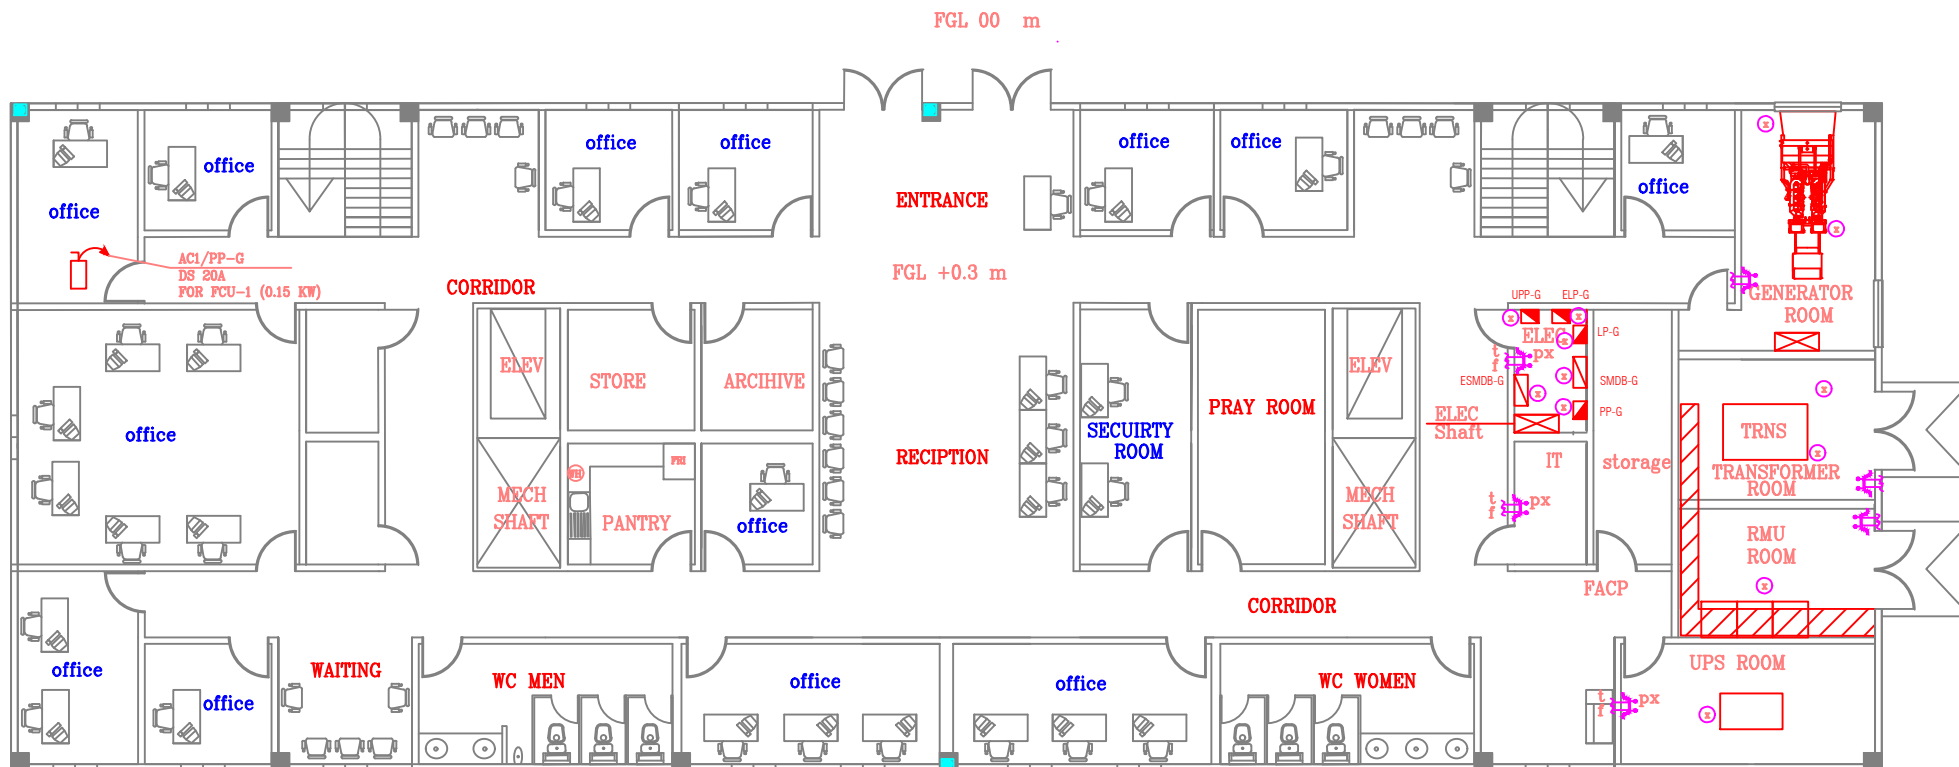

## Earthing and Lightning :

|  |                                                                                     |   |
|--|-------------------------------------------------------------------------------------|---|
|  |    | Earthing Rod with 3.6 lenght and 16 mm Diameter inside concret pit                                     |
|  |    | Test Link for Protective conductors connection                                                         |
|  |    | Earthing bare copper conductor XX mm2 direct buried under ground.                                      |
|  |   | Earthing copper conductor PVC insulated size as indicated on table                                     |
|  |  | BARE COPPER CONDUCTOR for lightning protection size as indicate on drawings                            |
|  |  | Insulated PVC COPPER CONDUCTOR for DOWN CONDUCTOR size as indicate on drawings                         |
|  |  | Insulated PVC COPPER CONDUCTOR for DOWN CONDUCTOR EMBEDDED ON COLUMN size as indicate on drawings      |
|  |  | COPPER AIR TERMINAL ROD FOR LIGHTNING PROTECTION HIGHT AND ANGLE OF PROTECTION as indicate on drawings |



